1935 发电厂 · 干煤棚公共化改造

初步一草 / 开放公共空间方案 01

ARCHITECTURE + LANDSCAPE

广州 · 荔湾 · 珠江东岸


01 设计概念

“煤仓变成城市客厅”

保留巨型柱列与屋面网架，将原煤棚内部改造成一条可穿行、可停留、可观江的公共街。

首层：地面公共街 + 绿化口袋

二层：空中展廊 + 餐饮平台 + 连续屋顶花园

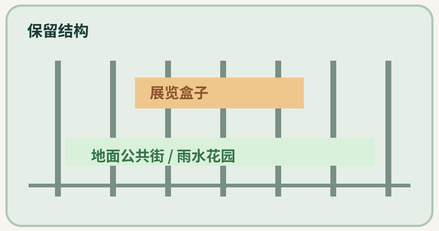


基准与暂定指标

建筑原长 × 宽	216m × 36m
结构模数	24 跨 × 9m
中部净空	约 18.5m
建议新增建筑面积	约 10,400㎡
绿化/可渗透目标	⩾ 35%（首轮）
公共开放面积目标	⩾ 40% 建筑面积


设计控制点

- 不触碰 A/B 轴柱列与屋面网架
- 首层形成东西贯通的公共主街
- 两端设无障碍入口，2 个主楼梯/电梯核心
- 南侧连续雨水花园，兼作遮阳与休憩边界
- 餐饮、展览可独立运营，夜间可分时开放

02 首层平面 / Ground floor 1:500（示意）

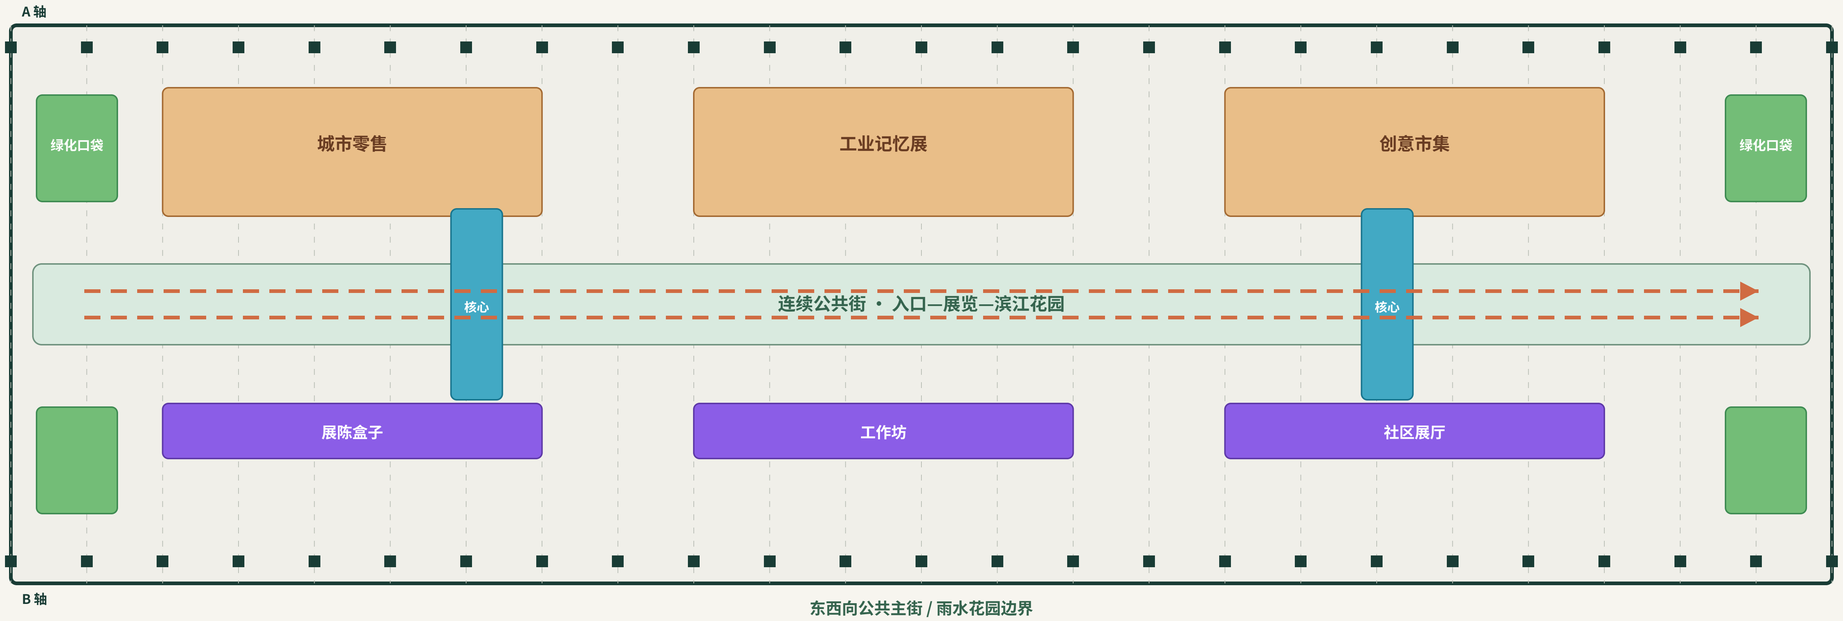

03 二层平面 / Level 2 1:500（示意）

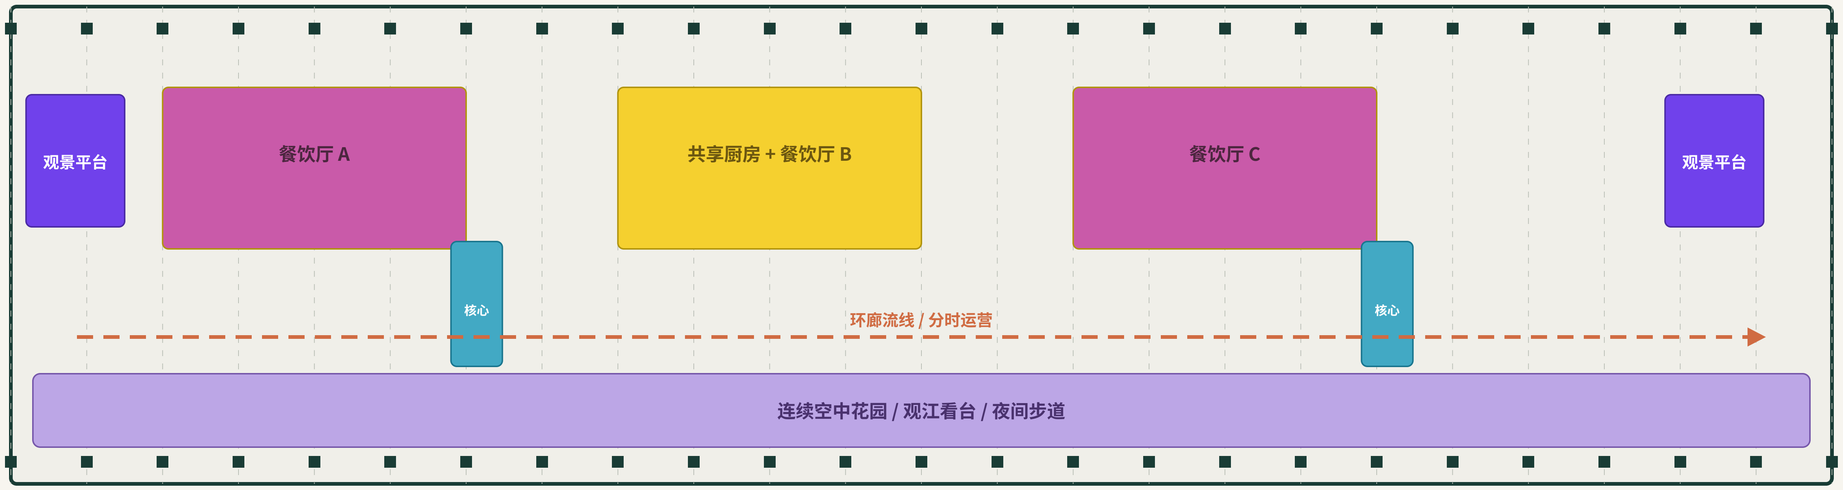

04 功能与流线图例

- 商业零售 / 市集
- 主题展览 / 工作坊
- 特色餐饮
- 共享厨房 / 活动厅
- 绿化口袋 / 雨水花园
- 楼梯、电梯、设备核
- 二层空中花园

流线策略

公众：两端入口 → 首层公共街 → 展览/零售 → 雨水花园；

餐饮：两侧核心上楼 → 二层环廊 → 餐饮平台/观江台；

后勤：北侧独立卸货带，避开公众主街；消防：两端+中部核心形成三段疏散。

说明：本图为基于任务书与 PSD 色块的概念性一草，尺寸以 216m×36m 柱网为控制；功能面积、消防分区、结构加固需在 CAD/BIM 阶段复核。